


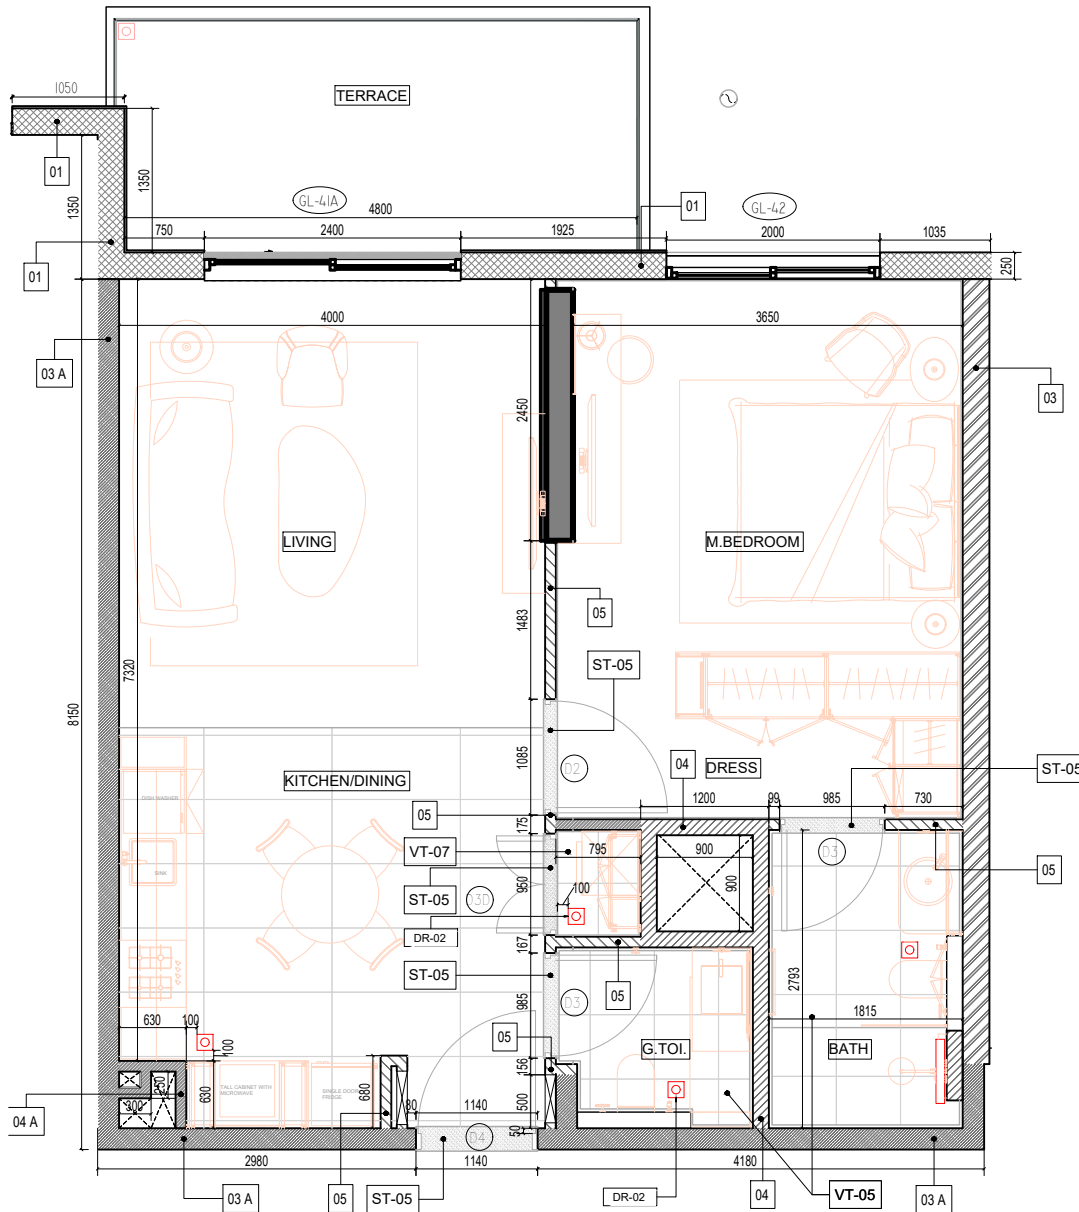

1 HILL 01 - LEVEL 1 - 1B A1-MASTER PLAN  
1:25

DOOR/ GLAZED DOOR SCHEDULE

| DOOR LEGEND | DOOR TYPE              | DIMENSIONS  |
|-------------|------------------------|-------------|
| D2          | SEMI SOLID FLUSH DOOR  | 1085 X 2223 |
| D3          | SOLID FLUSH/SEMI SOLID | 985 X 2223  |
| D3D         | SEMI SOLID FOLDING     | 950 X 2223  |
| D4          | SOLID FLUSH DOOR       | 1140 X 2223 |
| GL 41A      | WDW SLIDING DOOR       | 2400 X 2400 |
| GL 42       | WDW SLIDING DOOR       | 2000 X 2400 |

WALL TYPE SCHEDULE

| WALL TYPE CATEGORY | WALL THICKNESS (MM) | WALL TYPE           |
|--------------------|---------------------|---------------------|
| 01                 | 250                 | INSULATED BLOCKWORK |
| 03                 | 250                 | SOLID BLOCKWORK     |
| 03 A               | 200                 | SOLID BLOCKWORK     |
| 04                 | 150                 | SOLID BLOCKWORK     |
| 04 A               | 100                 | SOLID BLOCKWORK     |
| 05                 | 100                 | AAC BLOCK           |

FLOOR DRAIN TYPE

| LEGEND | DESCRIPTION         |
|--------|---------------------|
|        | FLOOR DRAIN         |
|        | LINEAR SHOWER DRAIN |

FLOOR FINISH LEGENDS

| LEGEND | DESCRIPTION         | SIZE       |
|--------|---------------------|------------|
| VT-01  | KITCHEN FLOOR TILE  | 1200 X 600 |
| VT-05  | BATHROOM FLOOR TILE | 600 X 600  |
| VT-07  | LAUNDRY FLOOR TILE  | 600 X 600  |
| ST-05  | STONE THRESHOLD     |            |

KEYPLAN:



NOTES:

DRAWINGS REFERENCE

| DOCUMENT REFERENCE NUMBER | REV | DESCRIPTION               |
|---------------------------|-----|---------------------------|
| H1-BLA-SC-SD-AR-L01-15001 | 0   | FOR BLOCKWORK REFERENCE   |
| H1-GEN-SC-SD-BW-L01-45007 | 0   | FOR FLOOR DRAIN REFERENCE |

DOCUMENT REVIEW

|     |                                         |         |
|-----|-----------------------------------------|---------|
| A   | APPROVED/REVIEWED AS NOTED              |         |
| B   | APPROVED/REVIEWED AS NOTED              |         |
| C   | REVISE & RESUBMIT. WORK MAY NOT PROCEED |         |
| D   | FOR INFORMATION/RECORD ONLY             |         |
| ENG | DATE                                    | RE DATE |

|                                              |                        |      |             |            |
|----------------------------------------------|------------------------|------|-------------|------------|
| DATUM LEVEL +13.00M. DMD<br>=+_0.00m. F.F.L. |                        |      |             |            |
| 00                                           | ISSUE FOR CONSTRUCTION | 2025 | EDCG        | WAS        |
| 01                                           | REV.00                 | 2025 |             |            |
| No                                           | Explanatory note       | Date | Prepared by | Checked by |

|             |                                                              |
|-------------|--------------------------------------------------------------|
| DEVELOPERS: | WASL<br>P.O. BOX 23073<br>DUBAI, UAE<br>TEL: +971(0)45116302 |
| CLIENT:     | جيه آيه جي العقارات ش. ذ. م. م.<br>J A G Real Estate L.L.C   |

|                  |                                             |
|------------------|---------------------------------------------|
| LEAD CONSULTANT: | EDCG<br>ENGINEERING DESIGN CONSULTING GROUP |
|------------------|---------------------------------------------|

|                 |                                                                                             |
|-----------------|---------------------------------------------------------------------------------------------|
| MEP CONSULTANT: | Ian Banhan & Associates<br>TEL: +97143102777 FAX: +97143105888<br>P.O. BOX 23061 DUBAI, UAE |
|-----------------|---------------------------------------------------------------------------------------------|

|                |                            |
|----------------|----------------------------|
| ED CONSULTANT: | interior design associates |
|----------------|----------------------------|

|                  |                     |
|------------------|---------------------|
| MAIN CONTRACTOR: | SALEH CONSTRUCTIONS |
|------------------|---------------------|

|                              |  |              |  |                                                                                             |  |        |  |
|------------------------------|--|--------------|--|---------------------------------------------------------------------------------------------|--|--------|--|
| Project Location :           |  |              |  | PROPOSED RESIDENTIAL BUILDING ON<br>PLOT-5919629, (HILL 01), JABAL ALI FIRST,<br>DUBAI, UAE |  |        |  |
| Location :                   |  |              |  | PLOT-5919629, JABAL ALI FIRST, DUBAI, UAE                                                   |  |        |  |
| Drawing Status :             |  |              |  | SHOP DRAWING                                                                                |  |        |  |
| Drawing Title :              |  |              |  | HILL 01 BUILDING A - FIRST FLOOR<br>1BA1-MASTERPLAN                                         |  |        |  |
| Prepared by :                |  | Checked by : |  | Scale :                                                                                     |  |        |  |
| RM                           |  | KA           |  | 1 : 25                                                                                      |  |        |  |
| Project No :                 |  | Date :       |  | Paper Size :                                                                                |  | Rev. : |  |
| P418                         |  | 05/DEC/2025  |  | A1                                                                                          |  | 00     |  |
| Drawing No :                 |  |              |  |                                                                                             |  |        |  |
| H1-BLA-SC-SD-AR-L01-15001-00 |  |              |  |                                                                                             |  |        |  |